


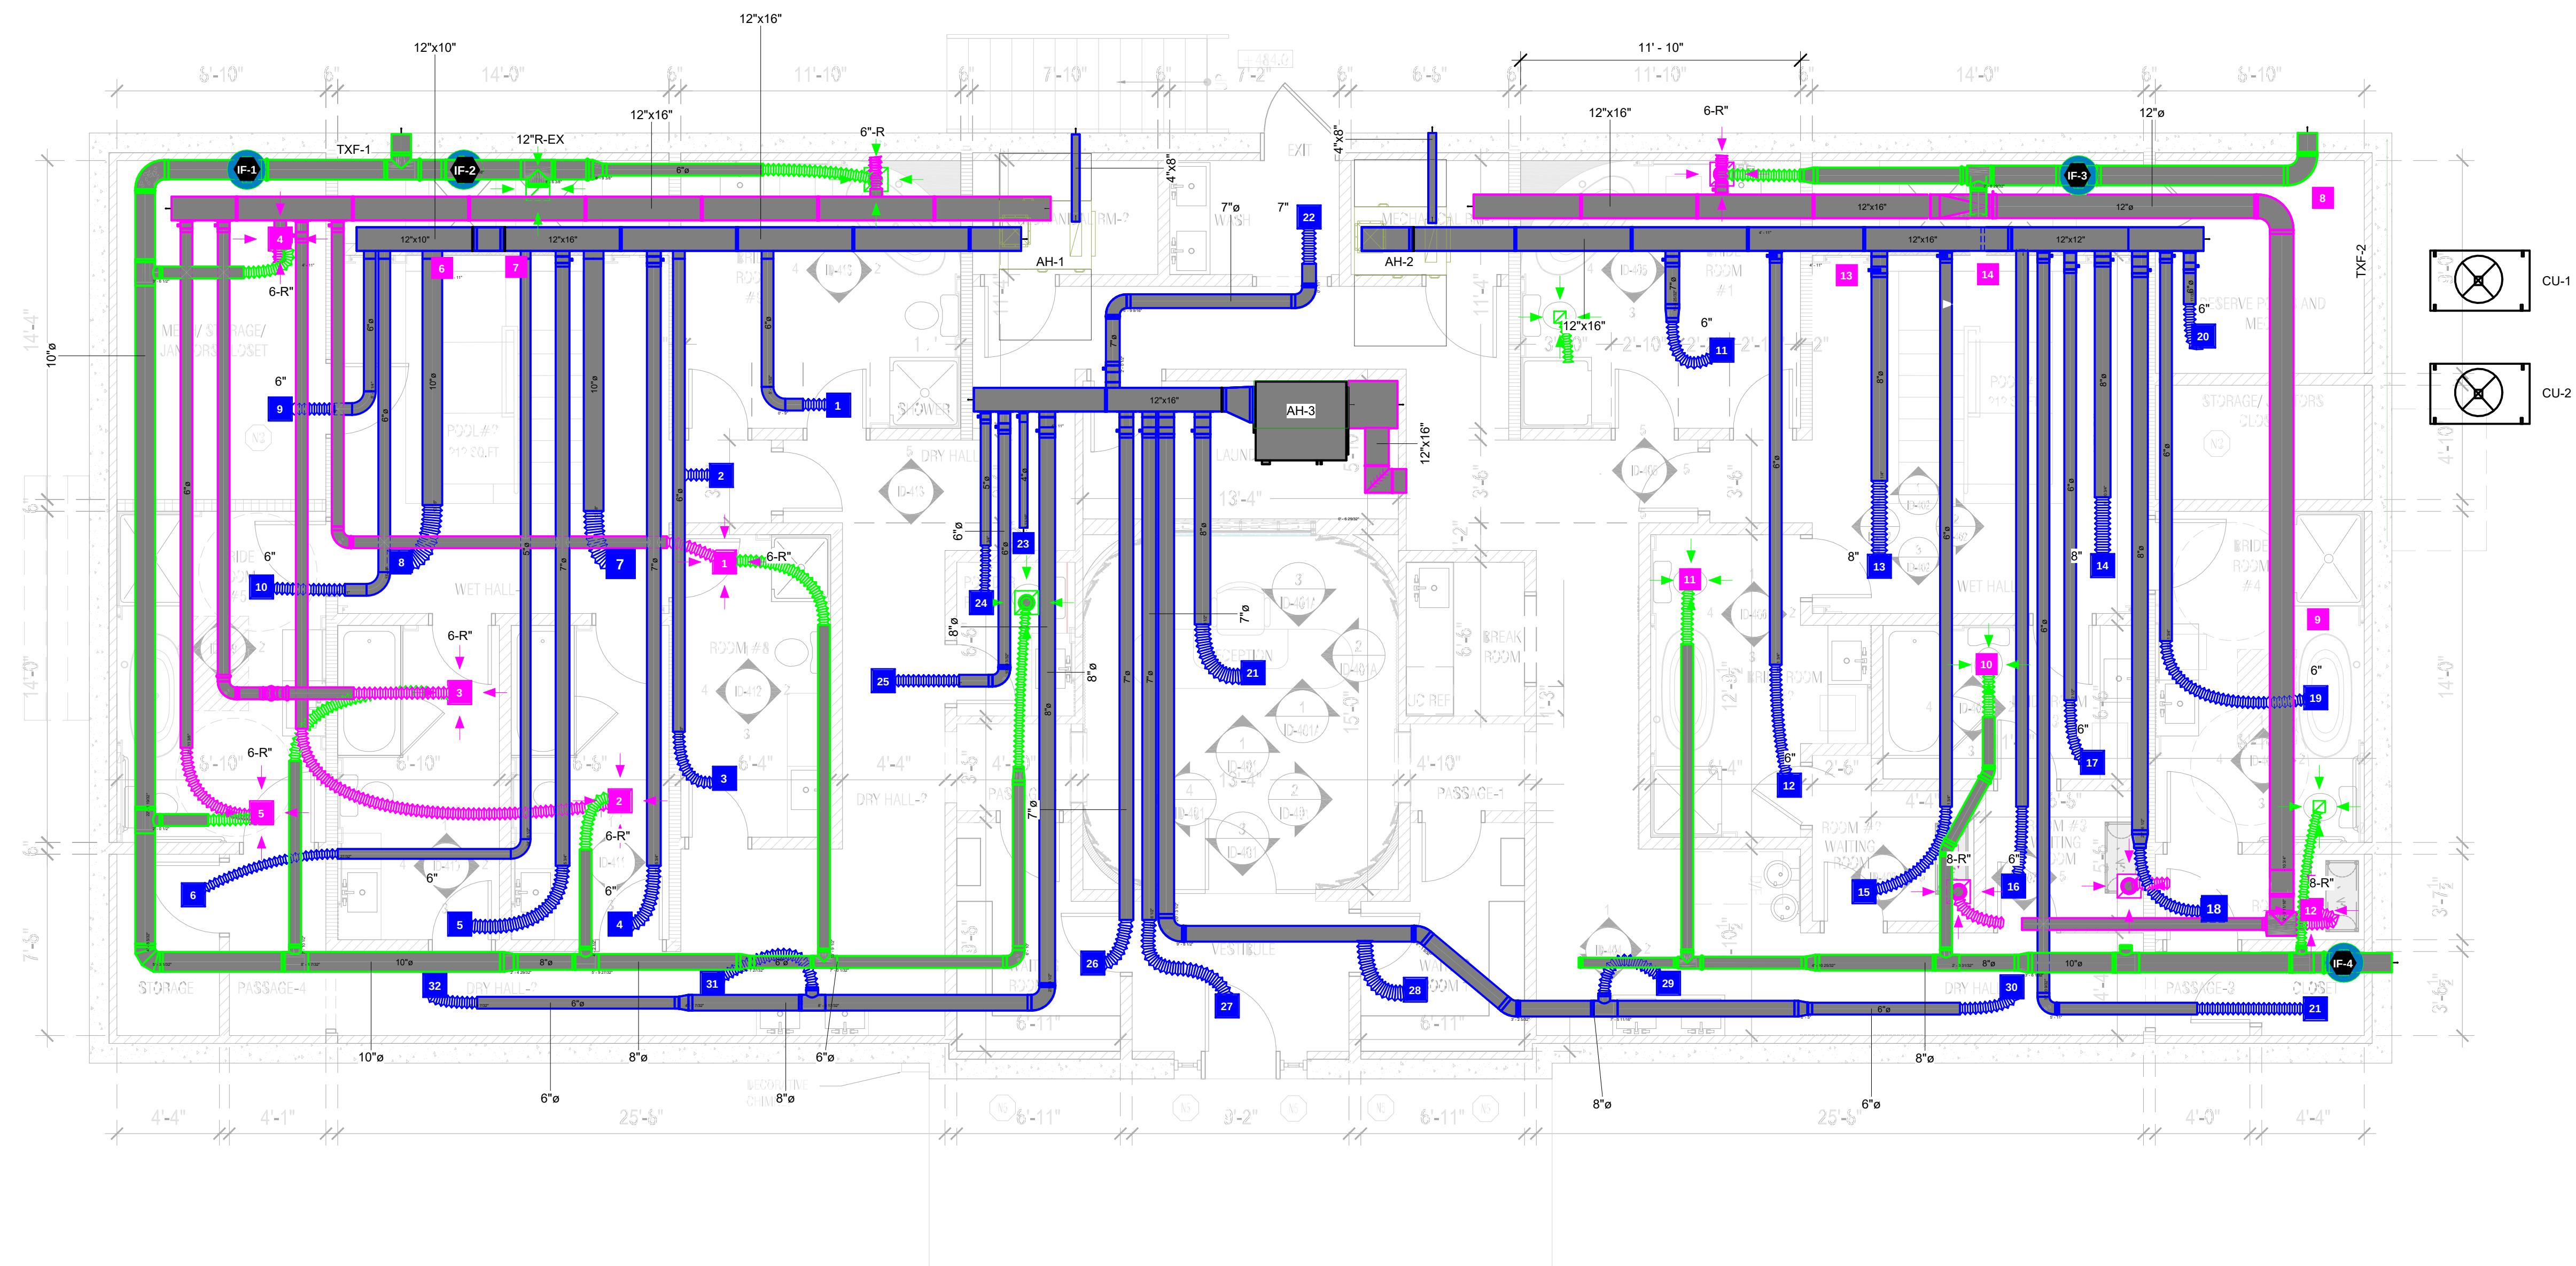

1 FIRST FLOOR LAYOUT
SCALE: 1/8" = 1'-0"

1 1st Floor
1/4" = 1'-0"